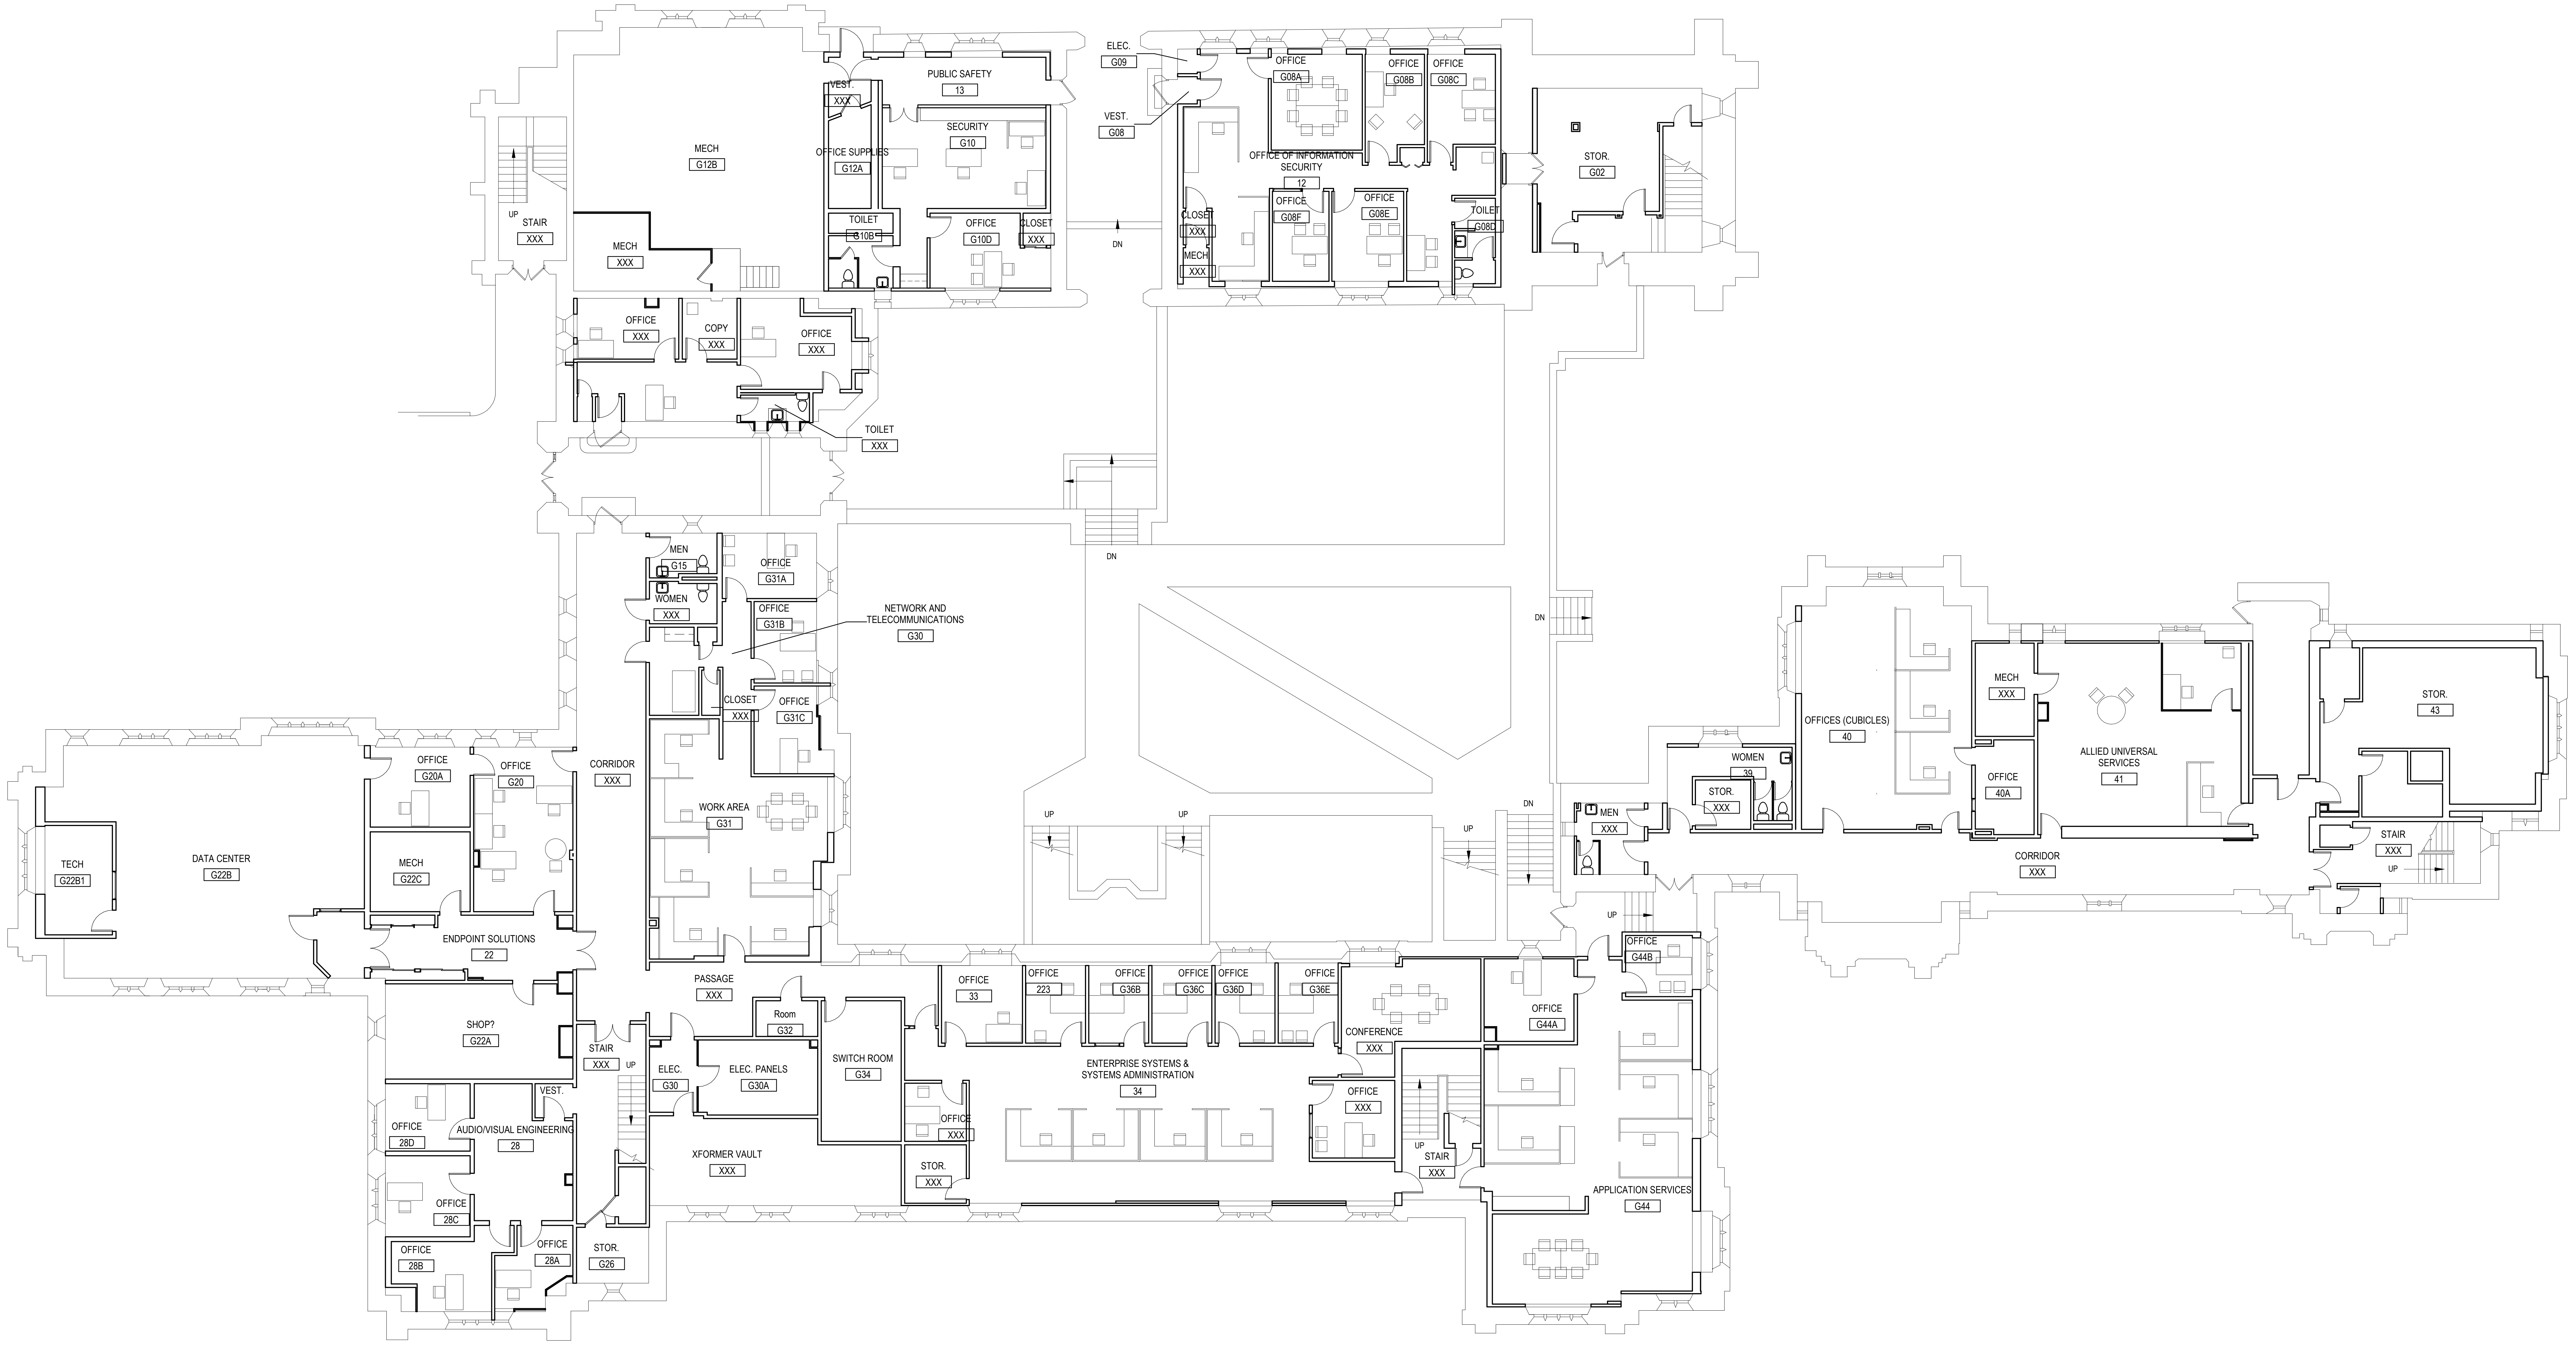

1
A1.00

GROUND FLOOR PLAN

3/32" = 1'-0"

NOTE: THIS DRAWING IS BASED UPON PLANS RECEIVED BY OUR OFFICE FROM THE BUILDING OWNER AND HAVE NOT BEEN FIELD MEASURED BY MEYER DESIGN INC. ACTUAL FIELD CONDITIONS MAY VARY.

MEYER
ARCHITECTURE + INTERIORS

MEYER DESIGN, INC. • MEYER ARCHITECTS, INC.
227 EAST LANCASTER AVENUE • ARDMORE, PA 19003-2304
VOICE • 610.649.8500 FAX • 610.649.8509
EMAIL • info @ meyerdesigninc.com

PRELIMINARY
NOT FOR CONSTRUCTION
MICHAEL STANCZAK
REGISTERED ARCHITECT
PA. REG# RA408583

SJU
Barbelin Hall
5600 CITY AVE
PHILADELPHIA, PA 19131

Township

GROUND FLOOR PLAN

REV. NO.	OPERATION	DATE	BY

SCALE:	3/32" = 1'-0"
JOB. NO.:	Project Number
PM:	PM
PROJECT NORTH	**DRAWING NO.**
	A1.00

3/17/2023 2:29:28 PM

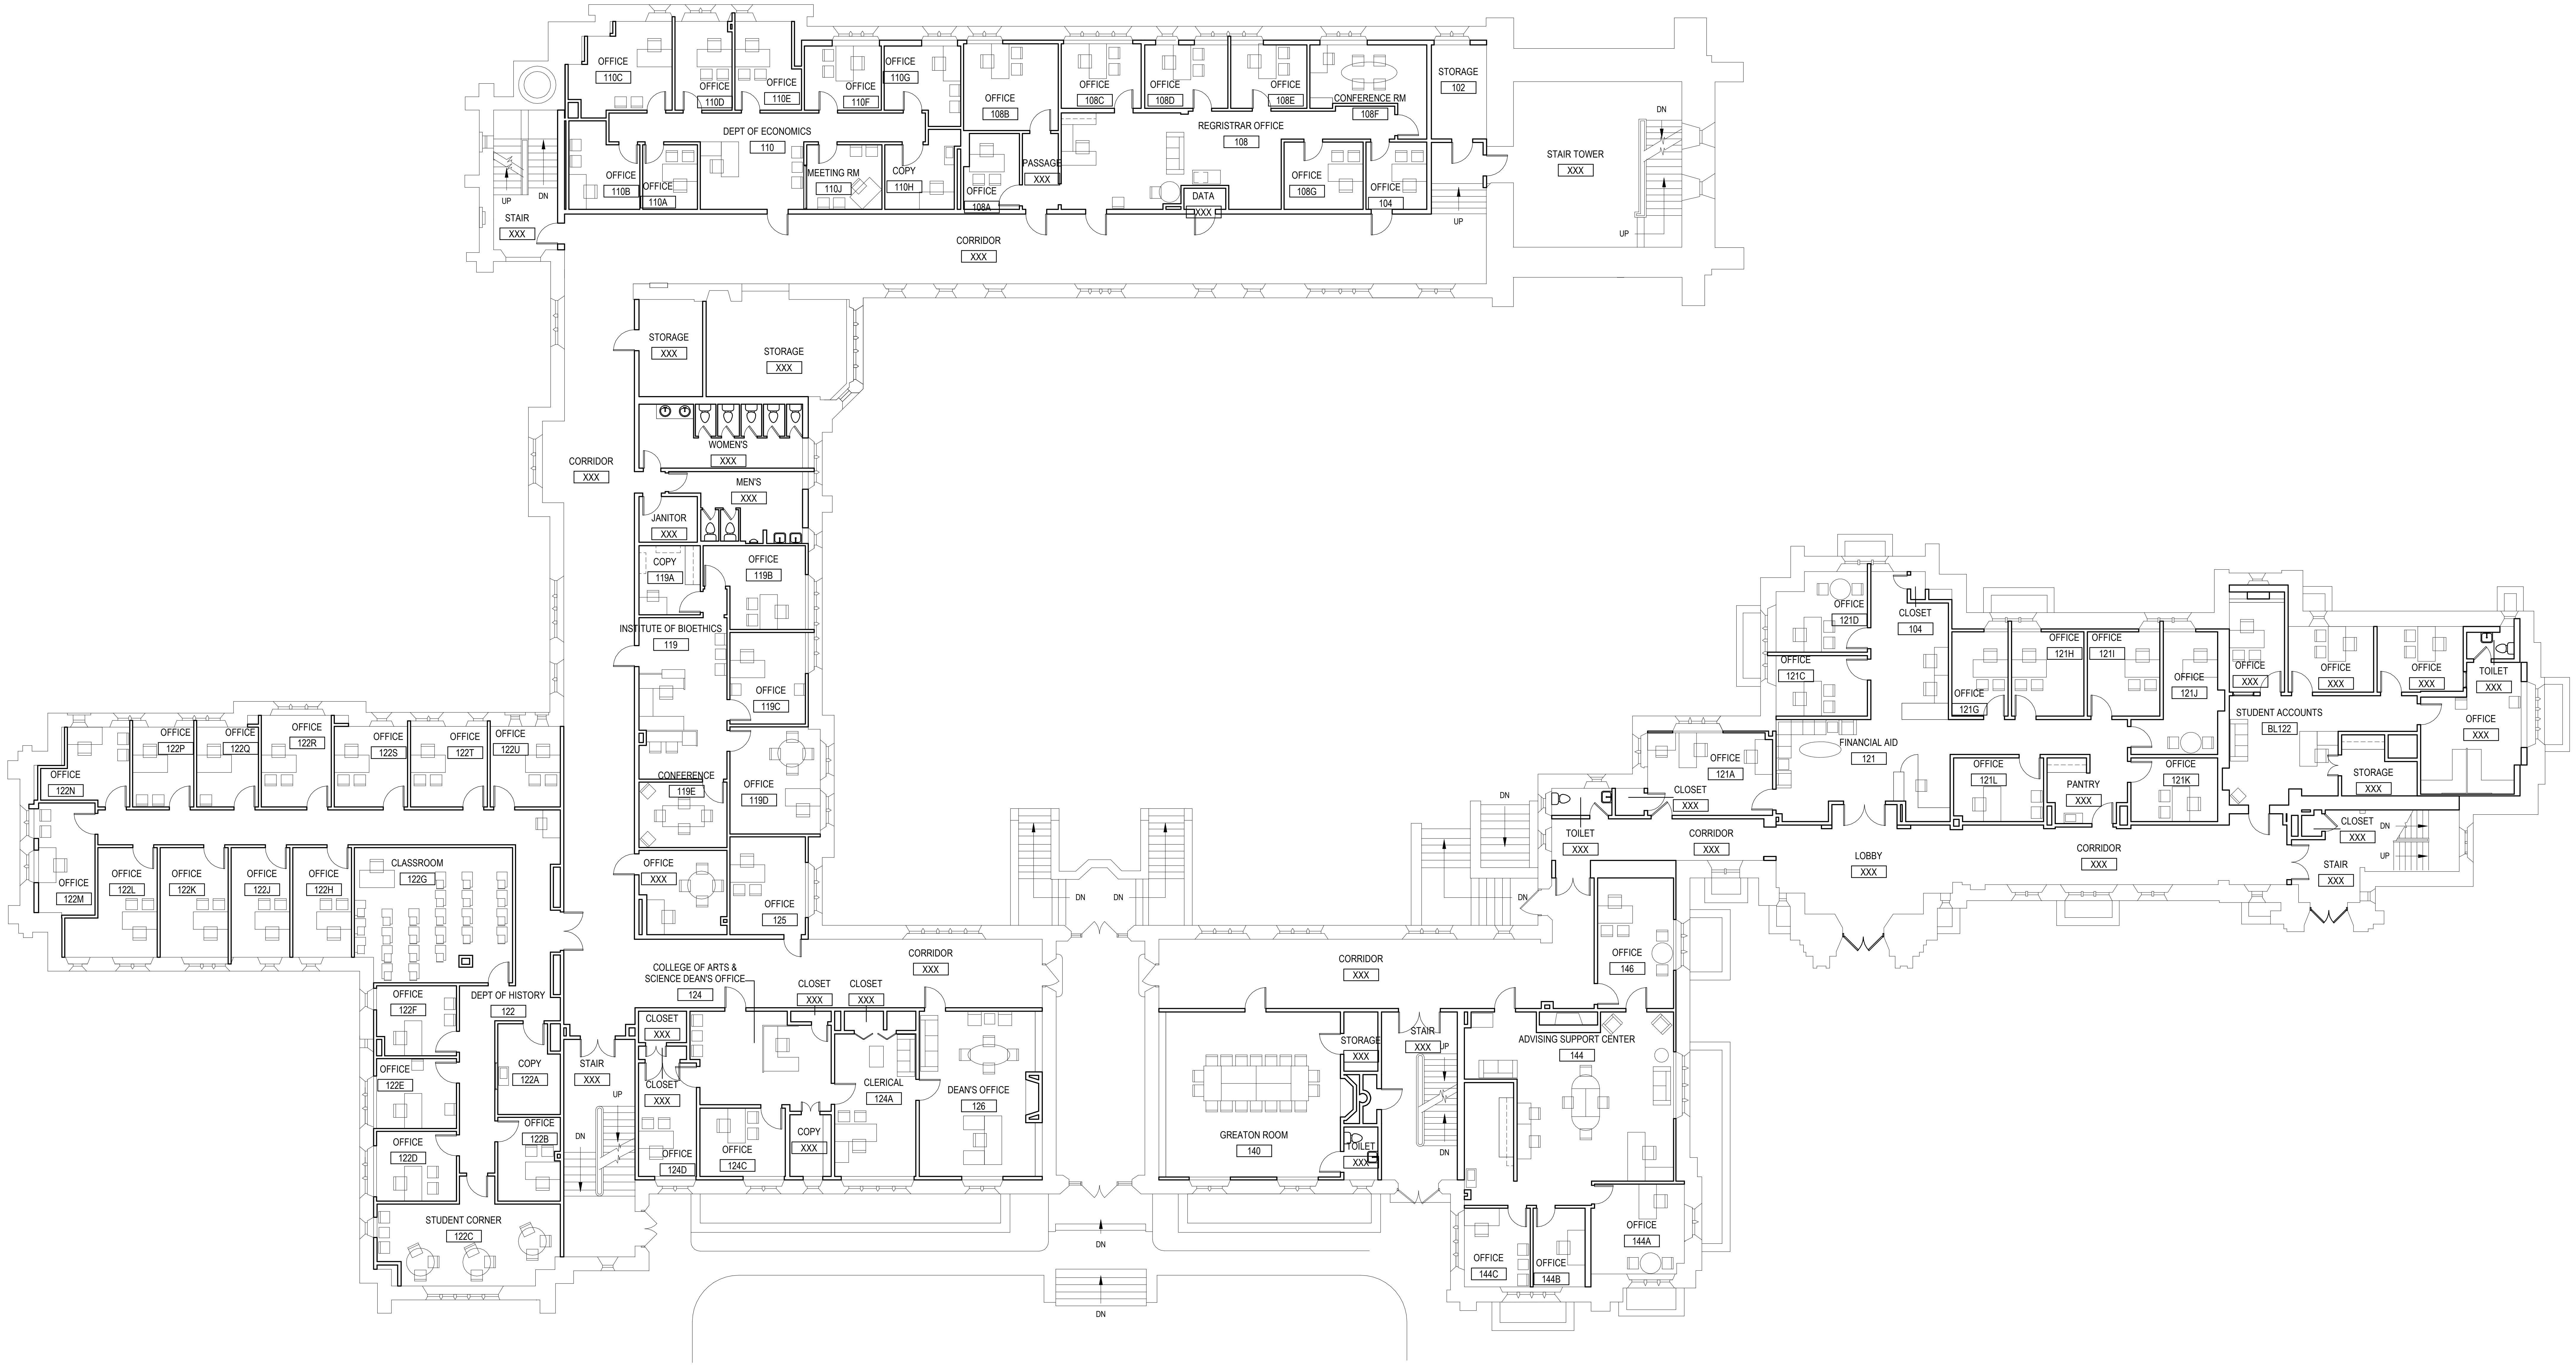

1
A1.01

FIRST FLOOR PLAN
3/32" = 1'-0"

NOTE: THIS DRAWING IS BASED UPON PLANS RECEIVED BY OUR OFFICE FROM THE BUILDING OWNER AND HAVE NOT BEEN FIELD MEASURED BY MEYER DESIGN INC. ACTUAL FIELD CONDITIONS MAY VARY.

MEYER
ARCHITECTURE + INTERIORS

MEYER DESIGN, INC. • MEYER ARCHITECTS, INC.
227 EAST LANCASTER AVENUE • ARDMORE, PA 19003-2304
VOICE • 610.649.8500 FAX • 610.649.8509
EMAIL • info @ meyerdesigninc.com

PRELIMINARY
NOT FOR CONSTRUCTION

MICHAEL STANCZAK
REGISTERED ARCHITECT
PA. REG# RA408583

SJU
Barbelin Hall
5600 CITY AVE
PHILADELPHIA, PA 19131

Township

FIRST FLOOR PLAN

REV. NO.	OPERATION	DATE	BY

SCALE:	3/32" = 1'-0"
JOB. NO.:	Project Number
PM:	PM
PROJECT NORTH	**DRAWING NO.**
	A1.01

3/17/2023 2:29:28 PM

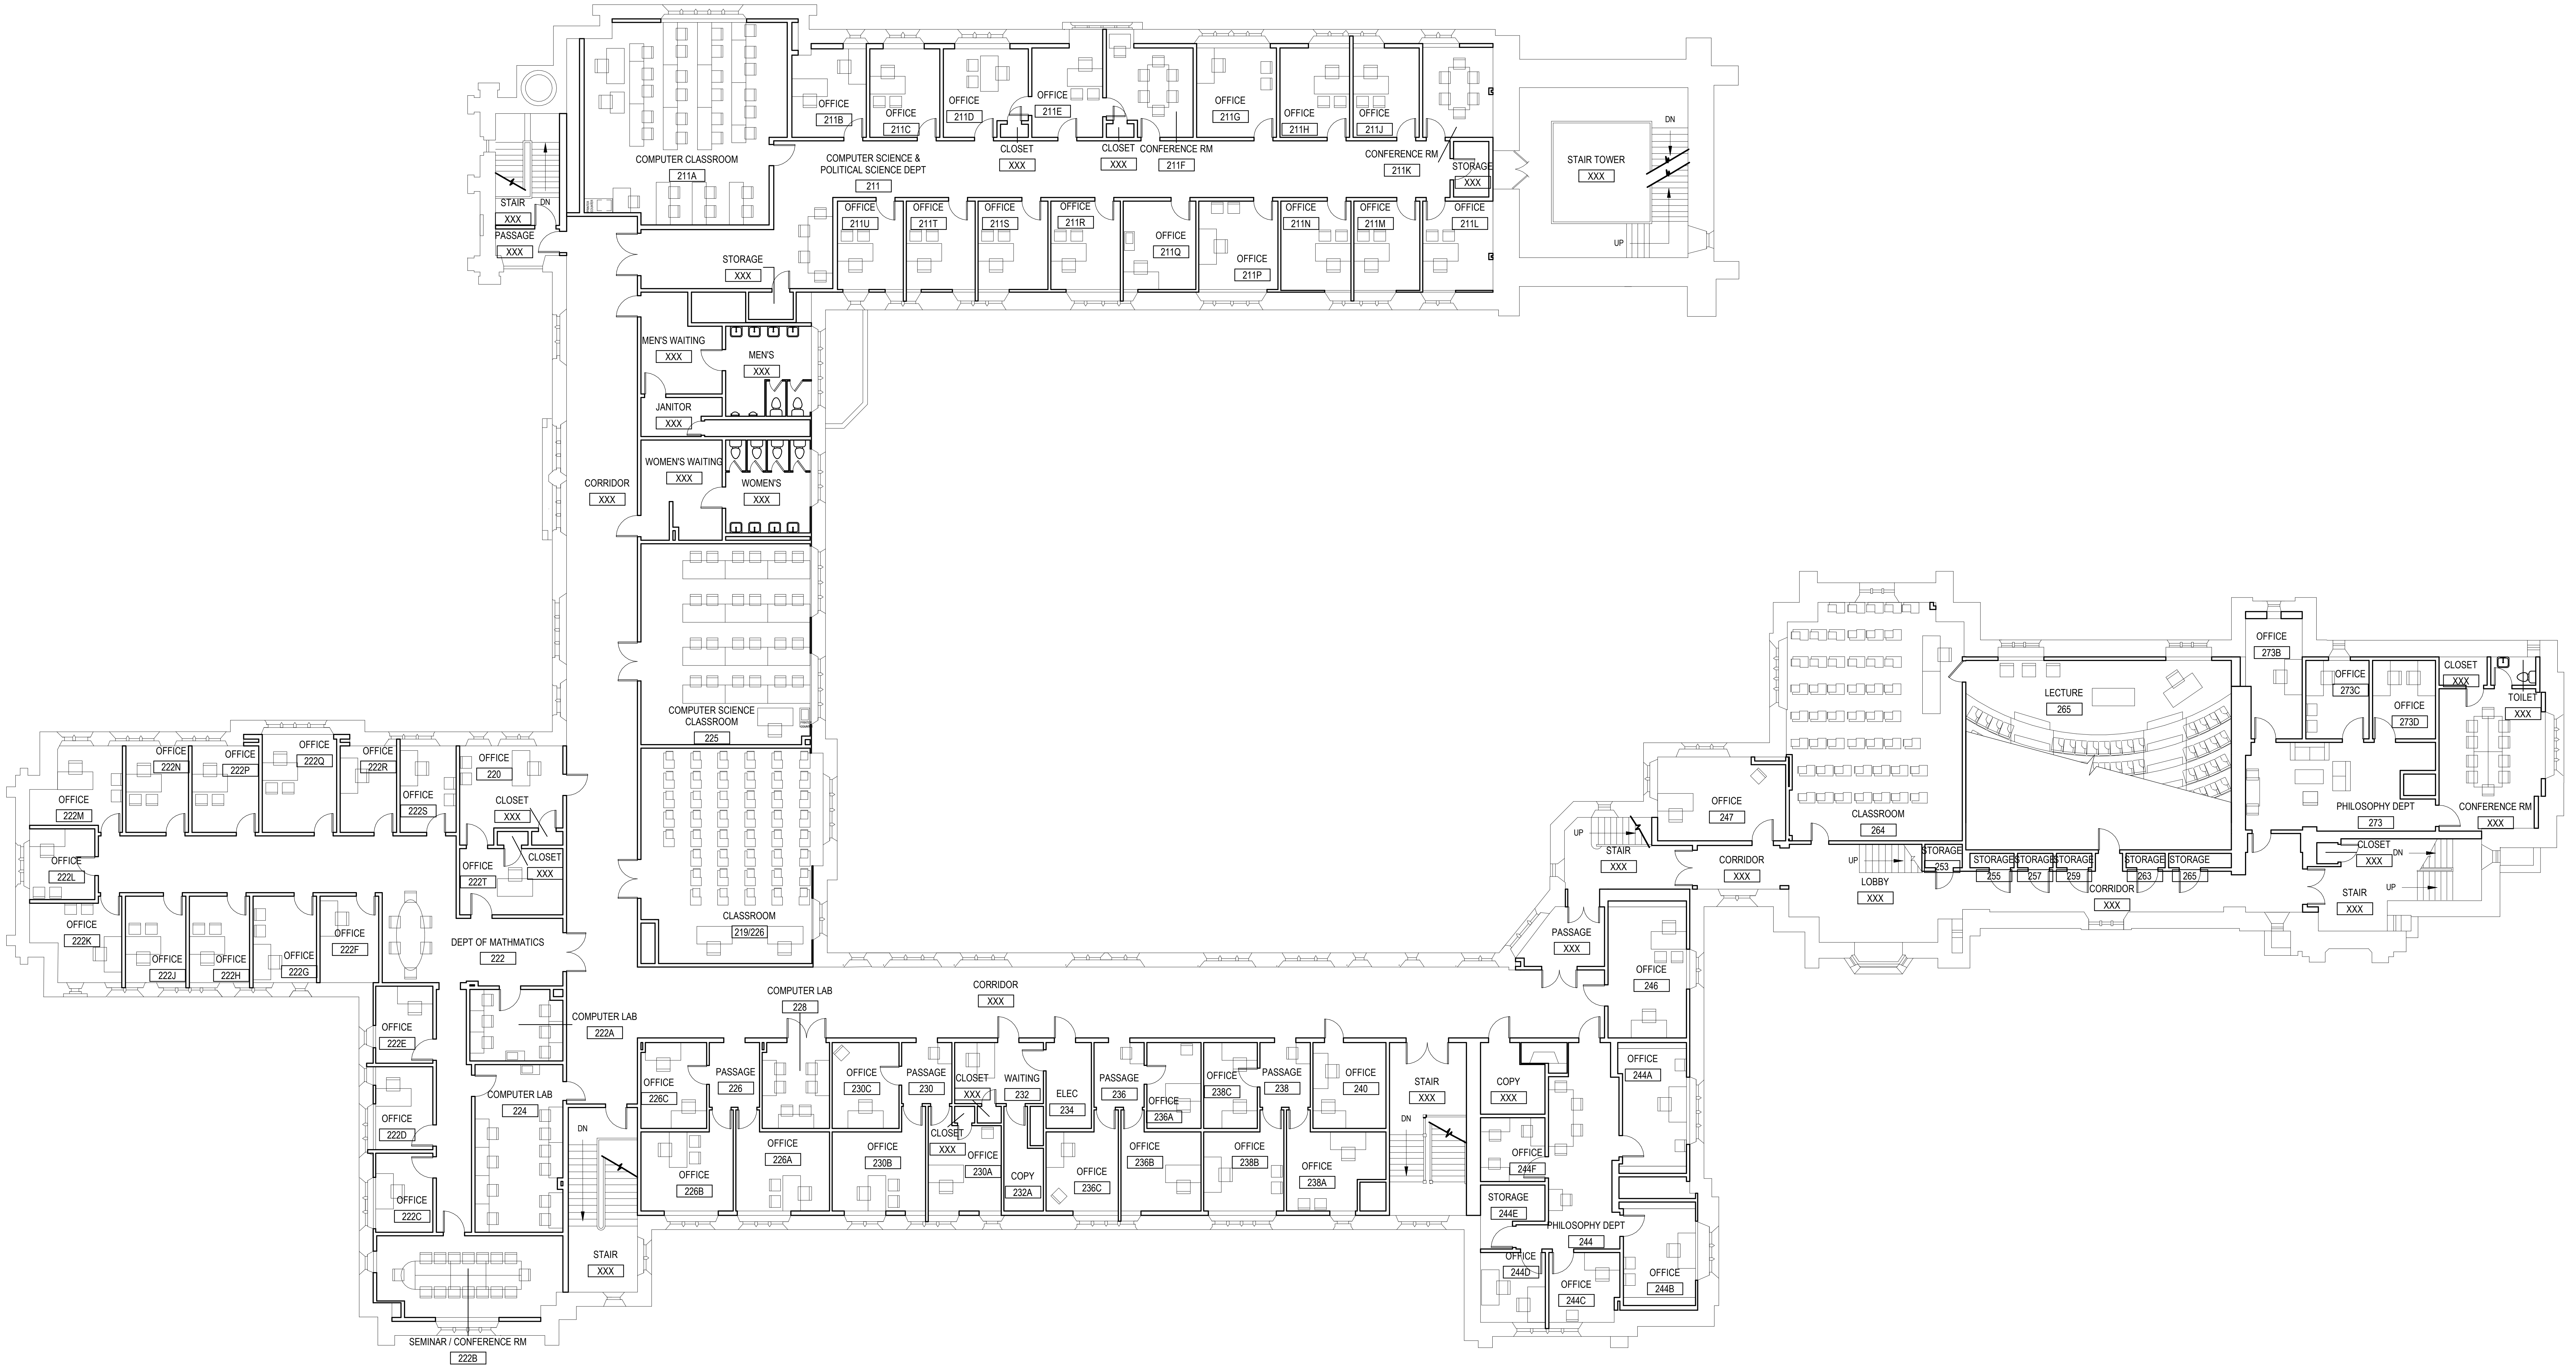

1
A1.02

SECOND FLOOR PLAN

3/32" = 1'-0"

NOTE: THIS DRAWING IS BASED UPON PLANS RECEIVED BY OUR OFFICE FROM THE BUILDING OWNER AND HAVE NOT BEEN FIELD MEASURED BY MEYER DESIGN INC. ACTUAL FIELD CONDITIONS MAY VARY.

MEYER
ARCHITECTURE + INTERIORS

MEYER DESIGN, INC. • MEYER ARCHITECTS, INC.
227 EAST LANCASTER AVENUE • ARDMORE, PA 19003-2304
VOICE • 610.649.8500 FAX • 610.649.8509
EMAIL • info @ meyerdesigninc.com

PRELIMINARY
NOT FOR
CONSTRUCTION

MICHAEL STANCZAK
REGISTERED ARCHITECT
PA. REG# RA408583

SJU
Barbelin Hall
5600 CITY AVE
PHILADELPHIA, PA 19131

Township

SECOND FLOOR PLAN

REV. NO.	OPERATION	DATE	BY

SCALE:	3/32" = 1'-0"
JOB. NO.:	Project Number
PM:	PM
PROJECT NORTH	**DRAWING NO.**
↑	**A1.02**

3/17/2023 2:29:29 PM

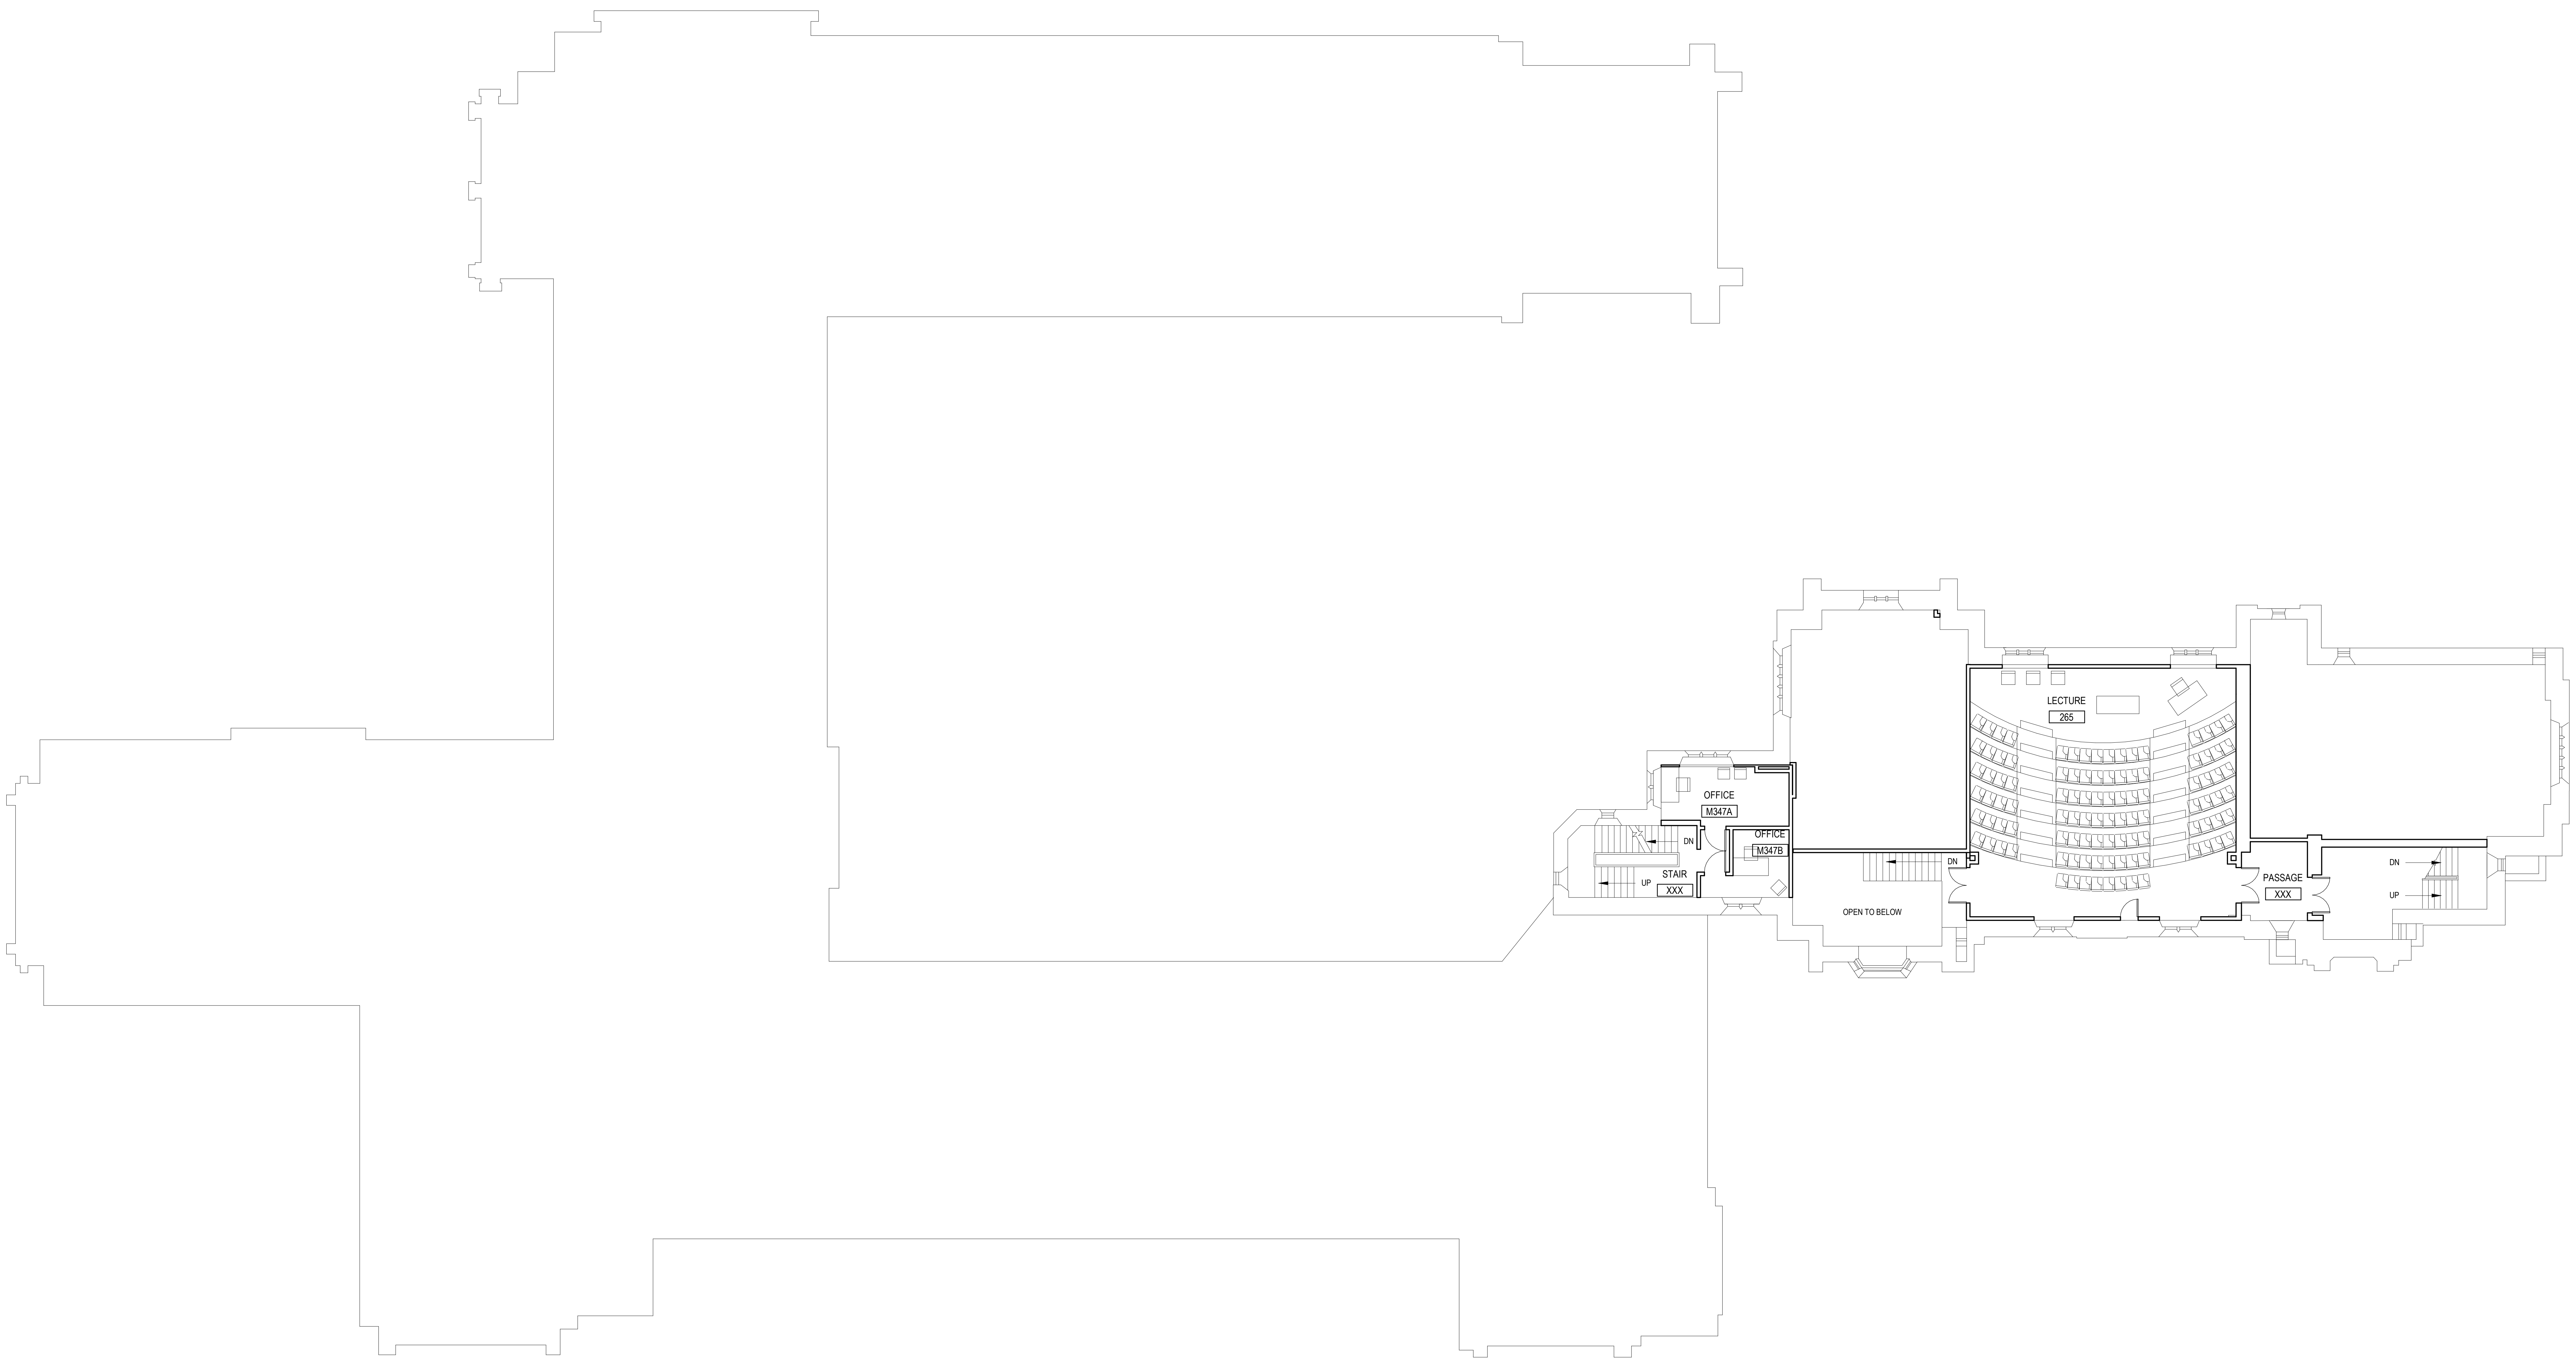

1
A1.02.5

MEZZANINE LEVEL PLAN

3/32" = 1'-0"

NOTE: THIS DRAWING IS BASED UPON PLANS RECEIVED BY OUR OFFICE FROM THE BUILDING OWNER AND HAVE NOT BEEN FIELD MEASURED BY MEYER DESIGN INC. ACTUAL FIELD CONDITIONS MAY VARY.

MEYER
ARCHITECTURE + INTERIORS

MEYER DESIGN, INC. • MEYER ARCHITECTS, INC.
227 EAST LANCASTER AVENUE • ARDMORE, PA 19003-2304
VOICE • 610.649.8500 FAX • 610.649.8509
EMAIL • info @ meyerdesigninc.com

PRELIMINARY

NOT FOR CONSTRUCTION

MICHAEL STANCZAK
REGISTERED ARCHITECT
PA. REG# RA408583

SJU
Barbelin Hall
5600 CITY AVE
PHILADELPHIA, PA 19131
Township

MEZZANINE LEVEL PLAN

REV. NO.	OPERATION	DATE	BY

SCALE:	3/32" = 1'-0"
JOB. NO.:	Project Number
PM:	PM
PROJECT NORTH	**DRAWING NO.**
↑	**A1.02.5**

3/17/2023 2:29:29 PM

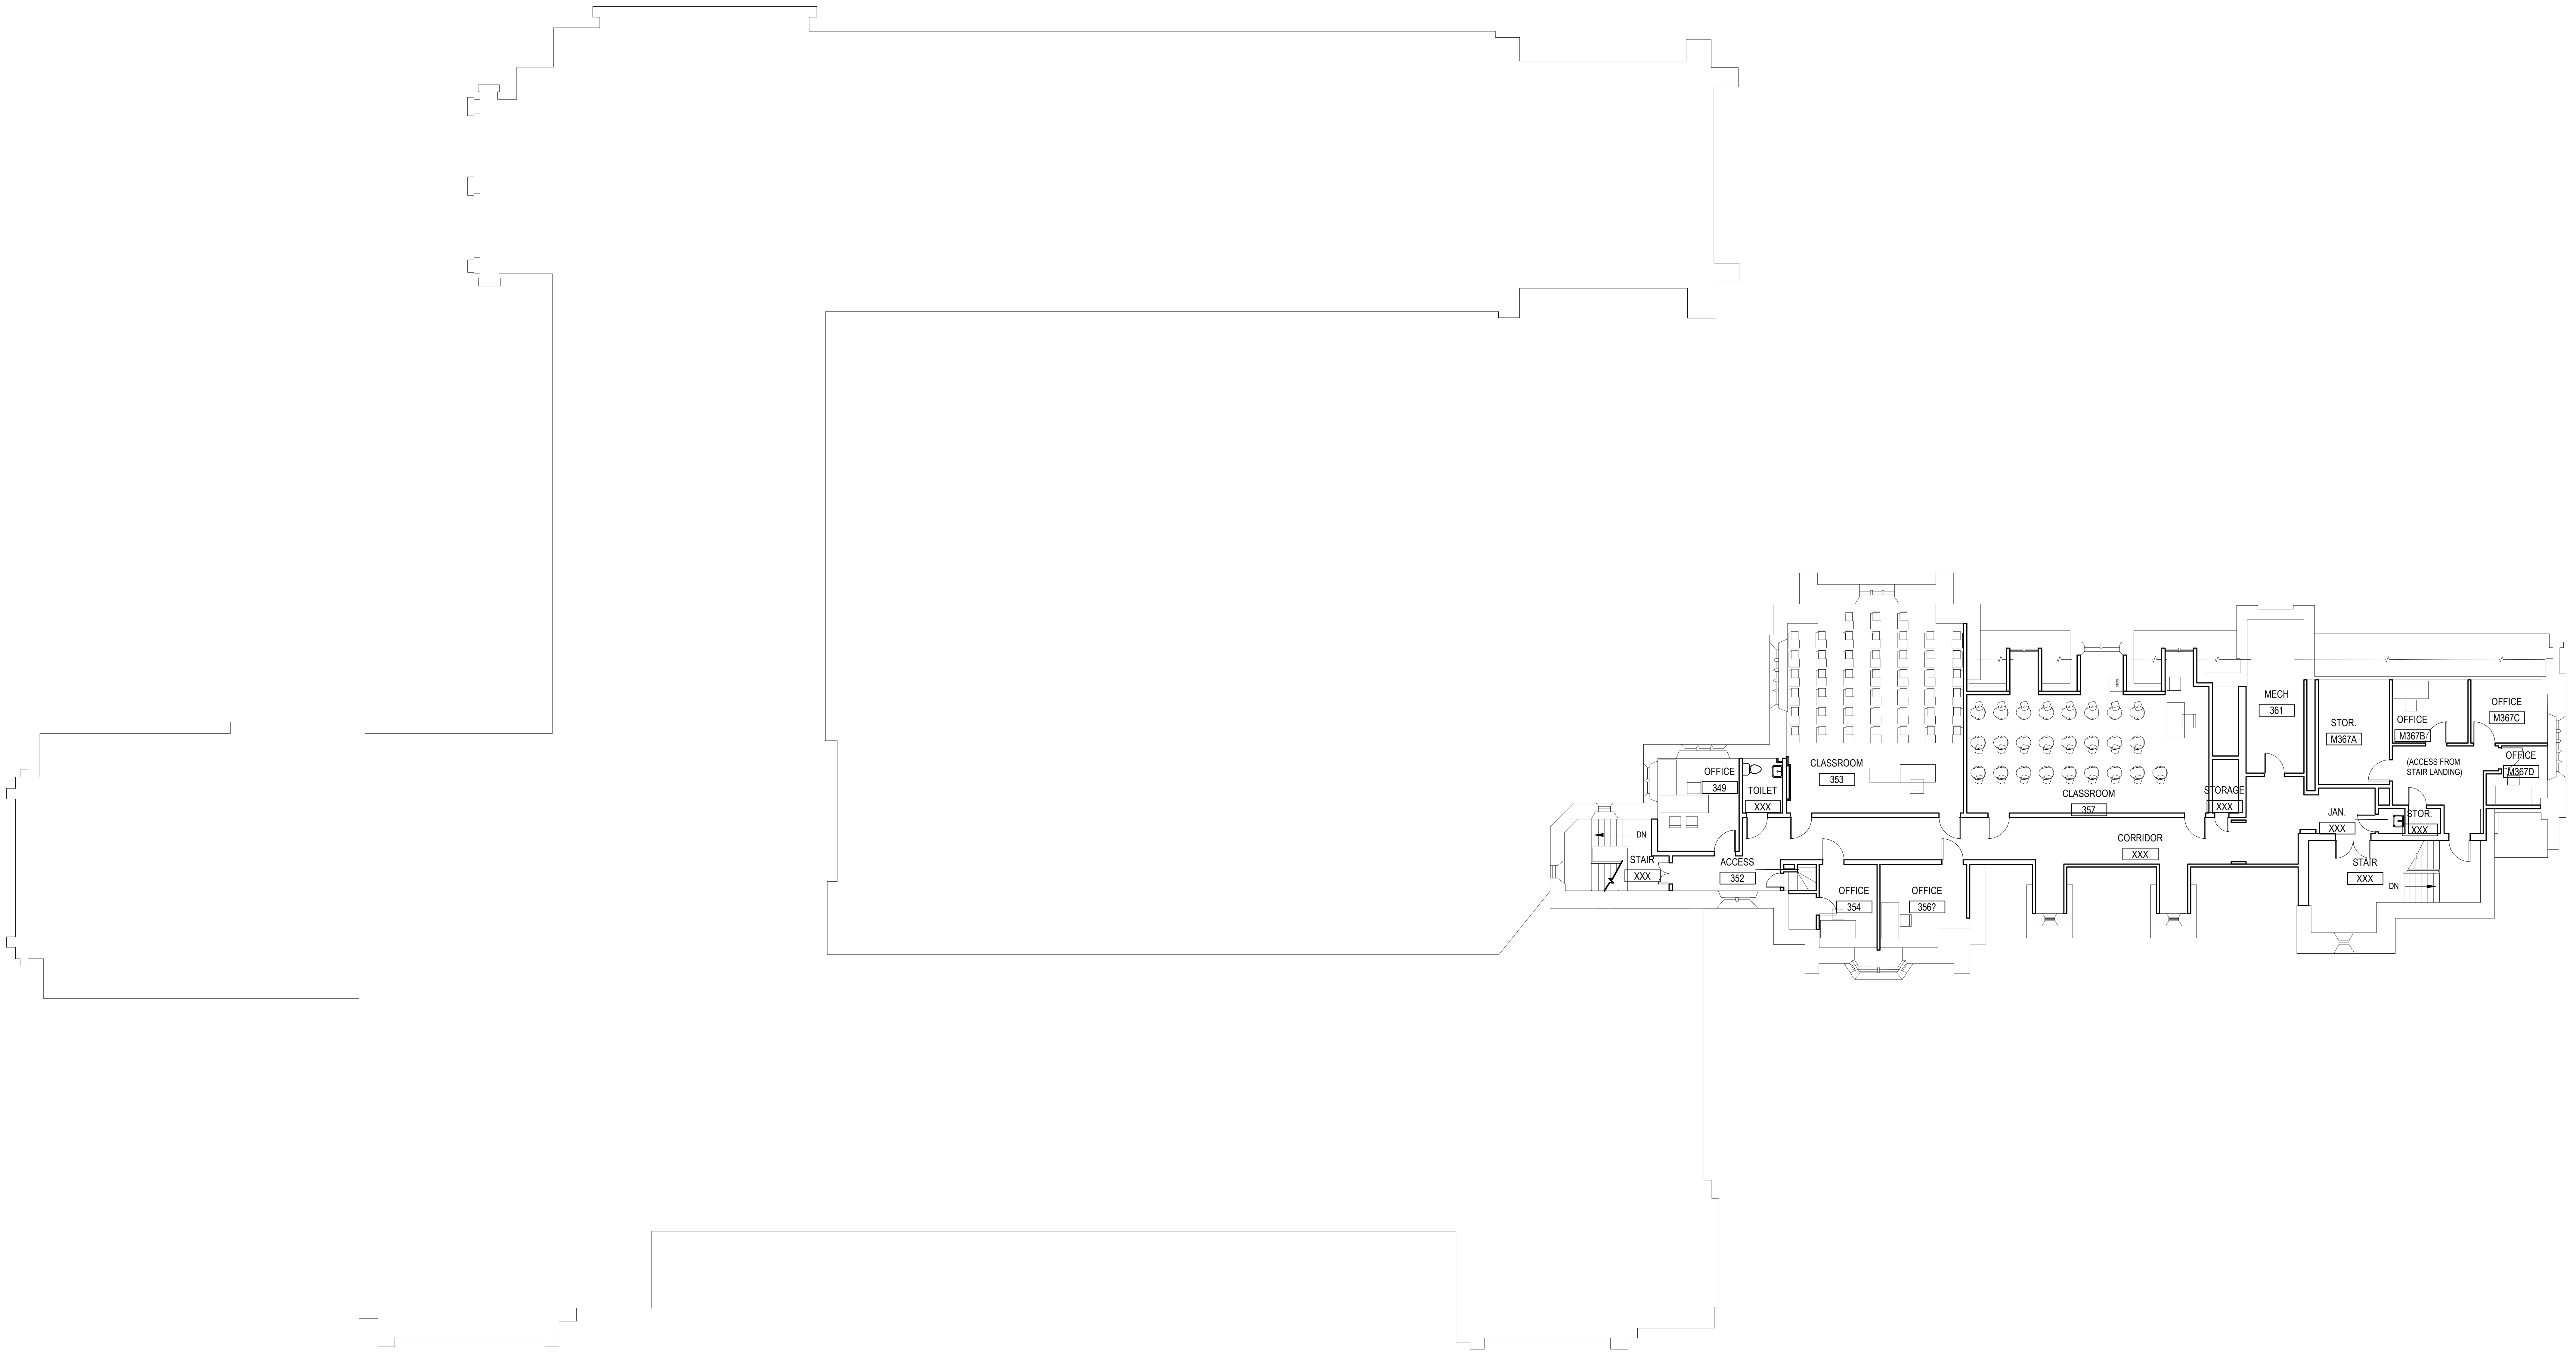

1
A1.03

THIRD FLOOR PLAN

3/32" = 1'-0"

NOTE: THIS DRAWING IS BASED UPON PLANS RECEIVED BY OUR OFFICE FROM THE BUILDING OWNER AND HAVE NOT BEEN FIELD MEASURED BY MEYER DESIGN INC. ACTUAL FIELD CONDITIONS MAY VARY.

MEYER
ARCHITECTURE + INTERIORS

MEYER DESIGN, INC. • MEYER ARCHITECTS, INC.
227 EAST LANCASTER AVENUE • ARDMORE, PA 19003-2304
VOICE • 610.649.8500 FAX • 610.649.8509
EMAIL • info@meyerdesigninc.com

PRELIMINARY

NOT FOR CONSTRUCTION

MICHAEL STANCZAK
REGISTERED ARCHITECT
PA. REG# RA408583

SJU
Barbelin Hall
5600 CITY AVE
PHILADELPHIA, PA 19131

Township

THIRD FLOOR PLAN

REV. NO.	OPERATION	DATE	BY

SCALE:	3/32" = 1'-0"
JOB. NO.:	Project Number
PM:	PM
PROJECT NORTH	**DRAWING NO.**
⬆	**A1.03**

3/17/2023 2:29:29 PM